
Furnished apartment plan

New Cairo · family of six · numbers match the room descriptions on page 2 · approx. 1:100 when printed on A4

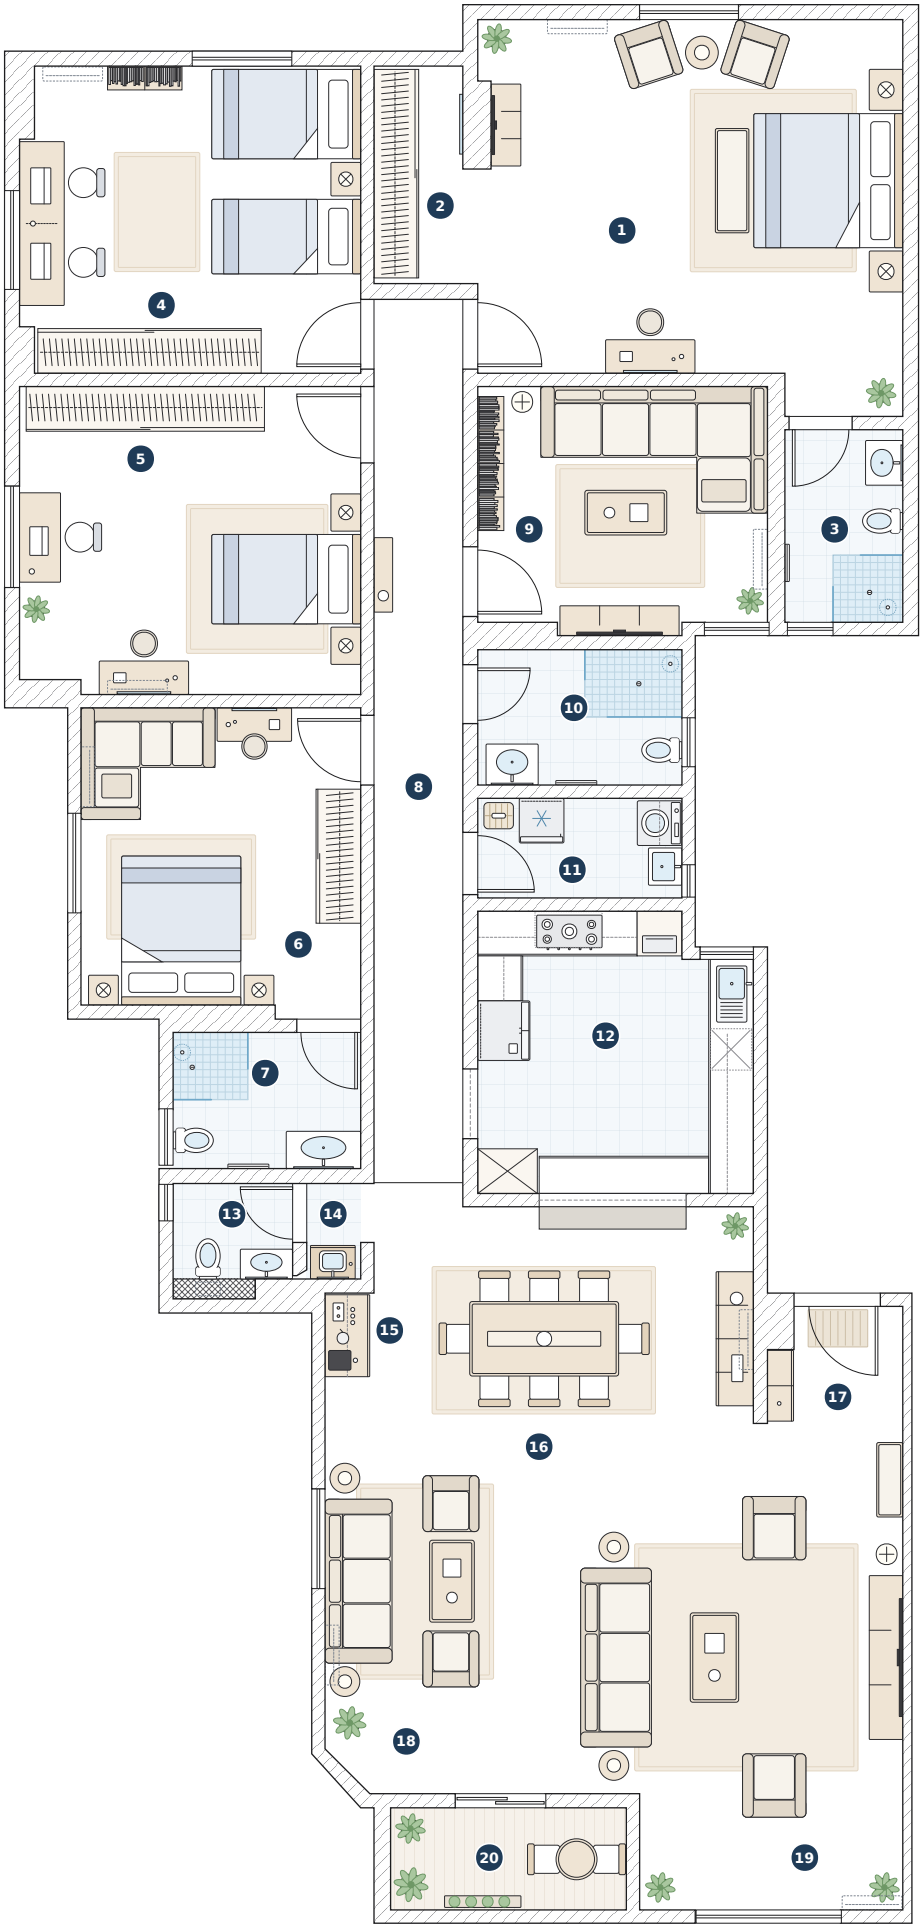

Dashed rectangles on walls = wall-mounted AC units · dashed lines in kitchen/laundry = wall cabinets/shelves · blue lines = shower glass
Cross-hatched block in the guest toilet = new built wall hiding the toilet cistern · all toilets are wall-hung

Room-by-room description

Positions read the plan as printed on page 1: **top, bottom, left, right** mean the top/bottom/left/right of the page. Numbers match the dark circles on the plan. Every toilet is wall-hung (cistern hidden in the wall) and every shower has glass walls. Ceilings are 3.25 m. AC sizes follow Sharp Egypt's room-size table (1.5 HP up to 12 m², 2.25 HP 13–18 m², 3 HP 19–24 m², 4 HP 25–31 m²), with each room's area increased by 16% for the higher ceiling; all are wall splits mounted at about 2.35 m, clear of tall furniture.

1. Parents' bedroom — King bed 180×200 with its headboard on the **right (outside) wall**, foot pointing left; a nightstand on each side and an upholstered bench across the foot. Two armchairs angled toward each other with a round side table between them, **under the top window**. TV unit (1.1 m) on the short wall stub at the **top-left**, facing the bed. Dressing table + stool on the **bottom wall** (shared with the family room), to the right of the corridor door. Rug under the lower two-thirds of the bed. Plants in the top-left corner and beside the bathroom door. **AC 5 HP** high on the top wall, left of the window, blowing down the room between the TV and the armchairs, not onto the bed.

2. Dressing area — 2.8 m sliding-door wardrobe along the whole **left wall** (shared with the brothers' room). Full-length mirror on the stub wall opposite it. About 0.6 m walkway, open to the bedroom.

3. Parents' bathroom — Door at the **top-left**, swinging in to rest against the left wall. **Right wall, top to bottom:** 60 cm vanity basin, then the wall-hung toilet, then a corner shower (≈0.95 × 0.9 m) in the **bottom-right corner** with glass on its top and left sides and the entry at the glass corner. **Left wall:** towel rail only (no storage unit). Window on the bottom wall, left of the shower.

4. Brothers' room (20 & 11) — Two single beds with headboards on the **right wall** (corridor/dressing side): 120×200 at the top for the older brother, 100×200 below it for the younger, one shared nightstand between them. Shared 2.2 m study desk along the **left wall, under the window**, with two desk chairs. 3.0 m wardrobe along the **bottom wall** (shared with room 5), stopping left of the door. Bookcase on the top wall, left of the window. Rug between the desk and the beds. **AC 3 HP** high on the top wall in the top-left corner, blowing toward the desks, not onto the beds.

5. Younger sister's room (16) — 120×200 bed with its headboard centred on the **right wall** (corridor side), a nightstand on each side. 3.2 m wardrobe along the **top wall** (shared with room 4), stopping left of the door. Desk + chair **under the left-wall window**; plant just below the desk. **AC 3 HP** high on the bottom wall above the dressing table, blowing up the room past the desk, not onto the bed. Dressing table + stool against the **bottom wall**, left of centre. Rug under the bed.

6. Older sister's room (23) — Door at the top of the **right wall**. Corner sofa (180 × 150 cm) in the **top-left corner**: long side along the top wall, short side down the left wall, ending at the window. Dressing table + stool on the **top wall**, right of the sofa, stopping before the open door. 160×200 bed with its headboard on the **bottom wall**, a nightstand on each side. 1.8 m sliding wardrobe on the **right wall**, starting just below the door (on your left as you walk in). Rug under the foot of the bed; ≈1.2 m between the bed and the sofa, ≈1.0 m between the bed and the wardrobe. **AC 2.25 HP** high on the left wall above the sofa, blowing across toward the wardrobe, not onto the bed. No desk.

7. Older sister's bathroom — Door at the **top-right**, swinging in to rest against the right wall. Shower 1.0 × 0.9 m in the **top-left corner** with two **short** glass panels: one on its right side (upper half) and one on the left half of its bottom side, leaving a wide open entry at the bottom-right corner. Wall-hung toilet on the **left wall under the window**. 1.0 m vanity in the **bottom-right corner**. No storage unit. Towel rail on the bottom wall.

8. Corridor — Kept clear except a slim 1.0 m console (25 cm deep) on the **left wall**, between the doors of rooms 5 and 6; 0.95 m stays free.

9. Family (TV) room — TV unit (1.6 m) set **into the niche in the bottom wall**. L-shaped sofa facing it: long side against the **top wall** (shared with the parents' bedroom), chaise running down the **right wall**. Coffee table in the middle on a rug. Tall bookcase on the **left wall above the door**; floor lamp between the bookcase and the sofa's left arm. Plant in the bottom-right corner by the window. **AC 2.25 HP** high on the right wall just below the chaise, blowing across the room in front of the sofa.

10. Main bathroom — Door at the **top-left**, swinging in to rest against the top wall. Shower (1.3 × 0.9 m) in the **top-right corner**, with a glass panel along its bottom side and a short return on its left side; entry at that corner. Wall-hung toilet on the **right wall under the window**, below the shower. Vanity basin in the **bottom-left corner** against the bottom wall. Towel rail on the bottom wall, middle. No bidet, no storage unit.

11. Laundry — Door at the bottom of the **left wall**. **Top wall, left to right:** dirty-clothes basket in the corner, then the upright deep freezer (60 × 60 cm); both clear of the door swing. **Right wall, top to bottom:** washing machine, then the small sink beside it, both facing the door, with a shelf above the washer. About 1 m of clear floor between the freezer and the washer.

12. Kitchen — **No door**: a framed opening in the left wall. **Top wall, left to right:** corner counter, counter with the 90 cm 5-burner built-in gas hob and a 90 cm hood above it (≈45 cm of worktop to its right before the oven unit, the corner worktop to its left), then the tall oven unit at the right end; wall cabinets above. **Left wall, top to bottom:** 60 cm of counter from the corner, then the fridge right before the opening; the fridge is on the opposite side of the kitchen from the oven, so neither door blocks the other. **Right wall, top to bottom:** one 60 cm-deep counter run from the window wall down to the bottom wall: the sink + drainer first, right beside the window, then the dishwasher directly below it, then worktop to the bottom wall; wall cabinets above, except over the sink so the window stays clear. **Bottom wall:** tall pantry in the bottom-left corner, just to your right as you enter, reaching to where the serving window starts; serving counter under the 2 m open hatch to the dining area: worktop at 90 cm, open up to 2.10 m, with a 30 cm ledge on the dining side; no stools. ≈2.4 m clear between the fridge and the right-hand counter.

13. Guest toilet — Entered from the outer-sink alcove through a door in its **right wall** (swings in against the top wall). New built wall along the **bottom** hides the cistern: wall-hung toilet against it in the left half, 70 cm basin beside it on the right. Window at the top of the left wall.

14. Outer sink — Vessel basin on a wood counter against the **bottom wall** of the alcove, mirror above; the alcove opens to the dining area on its right.

15. Coffee corner — 1.1 m counter against the **left wall of the reception**, directly below the outer-sink alcove: espresso machine, kettle, mugs, open shelves above.

16. Dining — Table 200 × 100 for 8 (3 chairs on each long side, 1 at each end), centred below the kitchen window, long side parallel to the kitchen wall, on a rug. 1.8 m sideboard on the **right wall** (back of the entrance wall). Plant in the top-right corner. **AC 2.25 HP** high above the sideboard, blowing along the table.

17. Entrance — Front door in the **top wall**, swinging in to rest against the right wall; doormat inside it. Shoe cabinet on the entrance's **left wall**. Bench on the **right wall**, moved down past the end of the entrance's left wall toward the TV seating, so the entrance stays ≈1.45 m clear.

18. Reception – formal salon — 3-seat sofa against the **left wall under the window**, coffee table in front, one armchair above and one below the table facing each other, round side tables at both sofa ends, rug. Plant in the angled corner below. **AC 4 HP** high on the left wall above the sofa, blowing across toward the TV seating.

19. Reception – TV seating — 2.2 m TV unit on the **right wall**. 3-seat sofa facing it in the middle of the room, side tables at both ends; coffee table between sofa and TV; one armchair above and one below, facing each other; rug. Floor lamp on the right wall above the TV unit. **AC 4 HP** high on the bottom wall right of the window, blowing up along the TV wall. Plants in the two bottom corners by the window.

20. Balcony — Sliding door in the **top wall**. Bistro table + 2 chairs on the **right side**; plants on the left; planter box along the bottom railing.